

מקרא וולבוקס

מיקום וולבוקס 

● מיקום מצלמה

WB MAIN A - 7 * ארון תקשורת 44U (חצר משק)

WB A - 1 * ארון תקשורת 15U (מצלמות ראשיות פלטפורמה)

WB B – 1 * ארון תקשורת 6U (מעבר שחקנים)

WB C - 4 * ארון רצפתי שקוע (פינות פרקט זירה)

WB D - 1 * ארון תקשורת 6U (קיר יציע מתקפל)

WB MAIN B - 4 * ארון תקשורת 44U (חדר תקשורת TV מפלס 0:0)

WB MAIN C - 1 * ארון תקשורת 44U (חדר תקשורת TV מפלס 16)

WB Z - 1 * ארון תקשורת 6U (חדר תקשורת TV קומה 0)

WB M - 1 * ארון תקשורת 6U (חדר בזק כניסה מהרחוב)

WB E - 1 * צינור ללא ארון (מצלמת BEAUTY)

WB P - 1 * צינור ללא ארון (מצלמת פיקסלוט)

WB F - 1 * ארון תקשורת 6U (תא צפייה / אולפן)


WB G - 1 * ארון תקשורת 6U (הלבשת שחקנים)

WB T - 1 * צינור ללא ארון (מצלמת TOP אמצע מגרש תקרה)

WB 1 - 1 * ארון תקשורת 6U (עיתונאים)

WB H - 1 * ארון תקשורת 6U (מנוחת שחקנים)

WB K - 1 * ארון תקשורת 15U (פינות פרקט זירה)

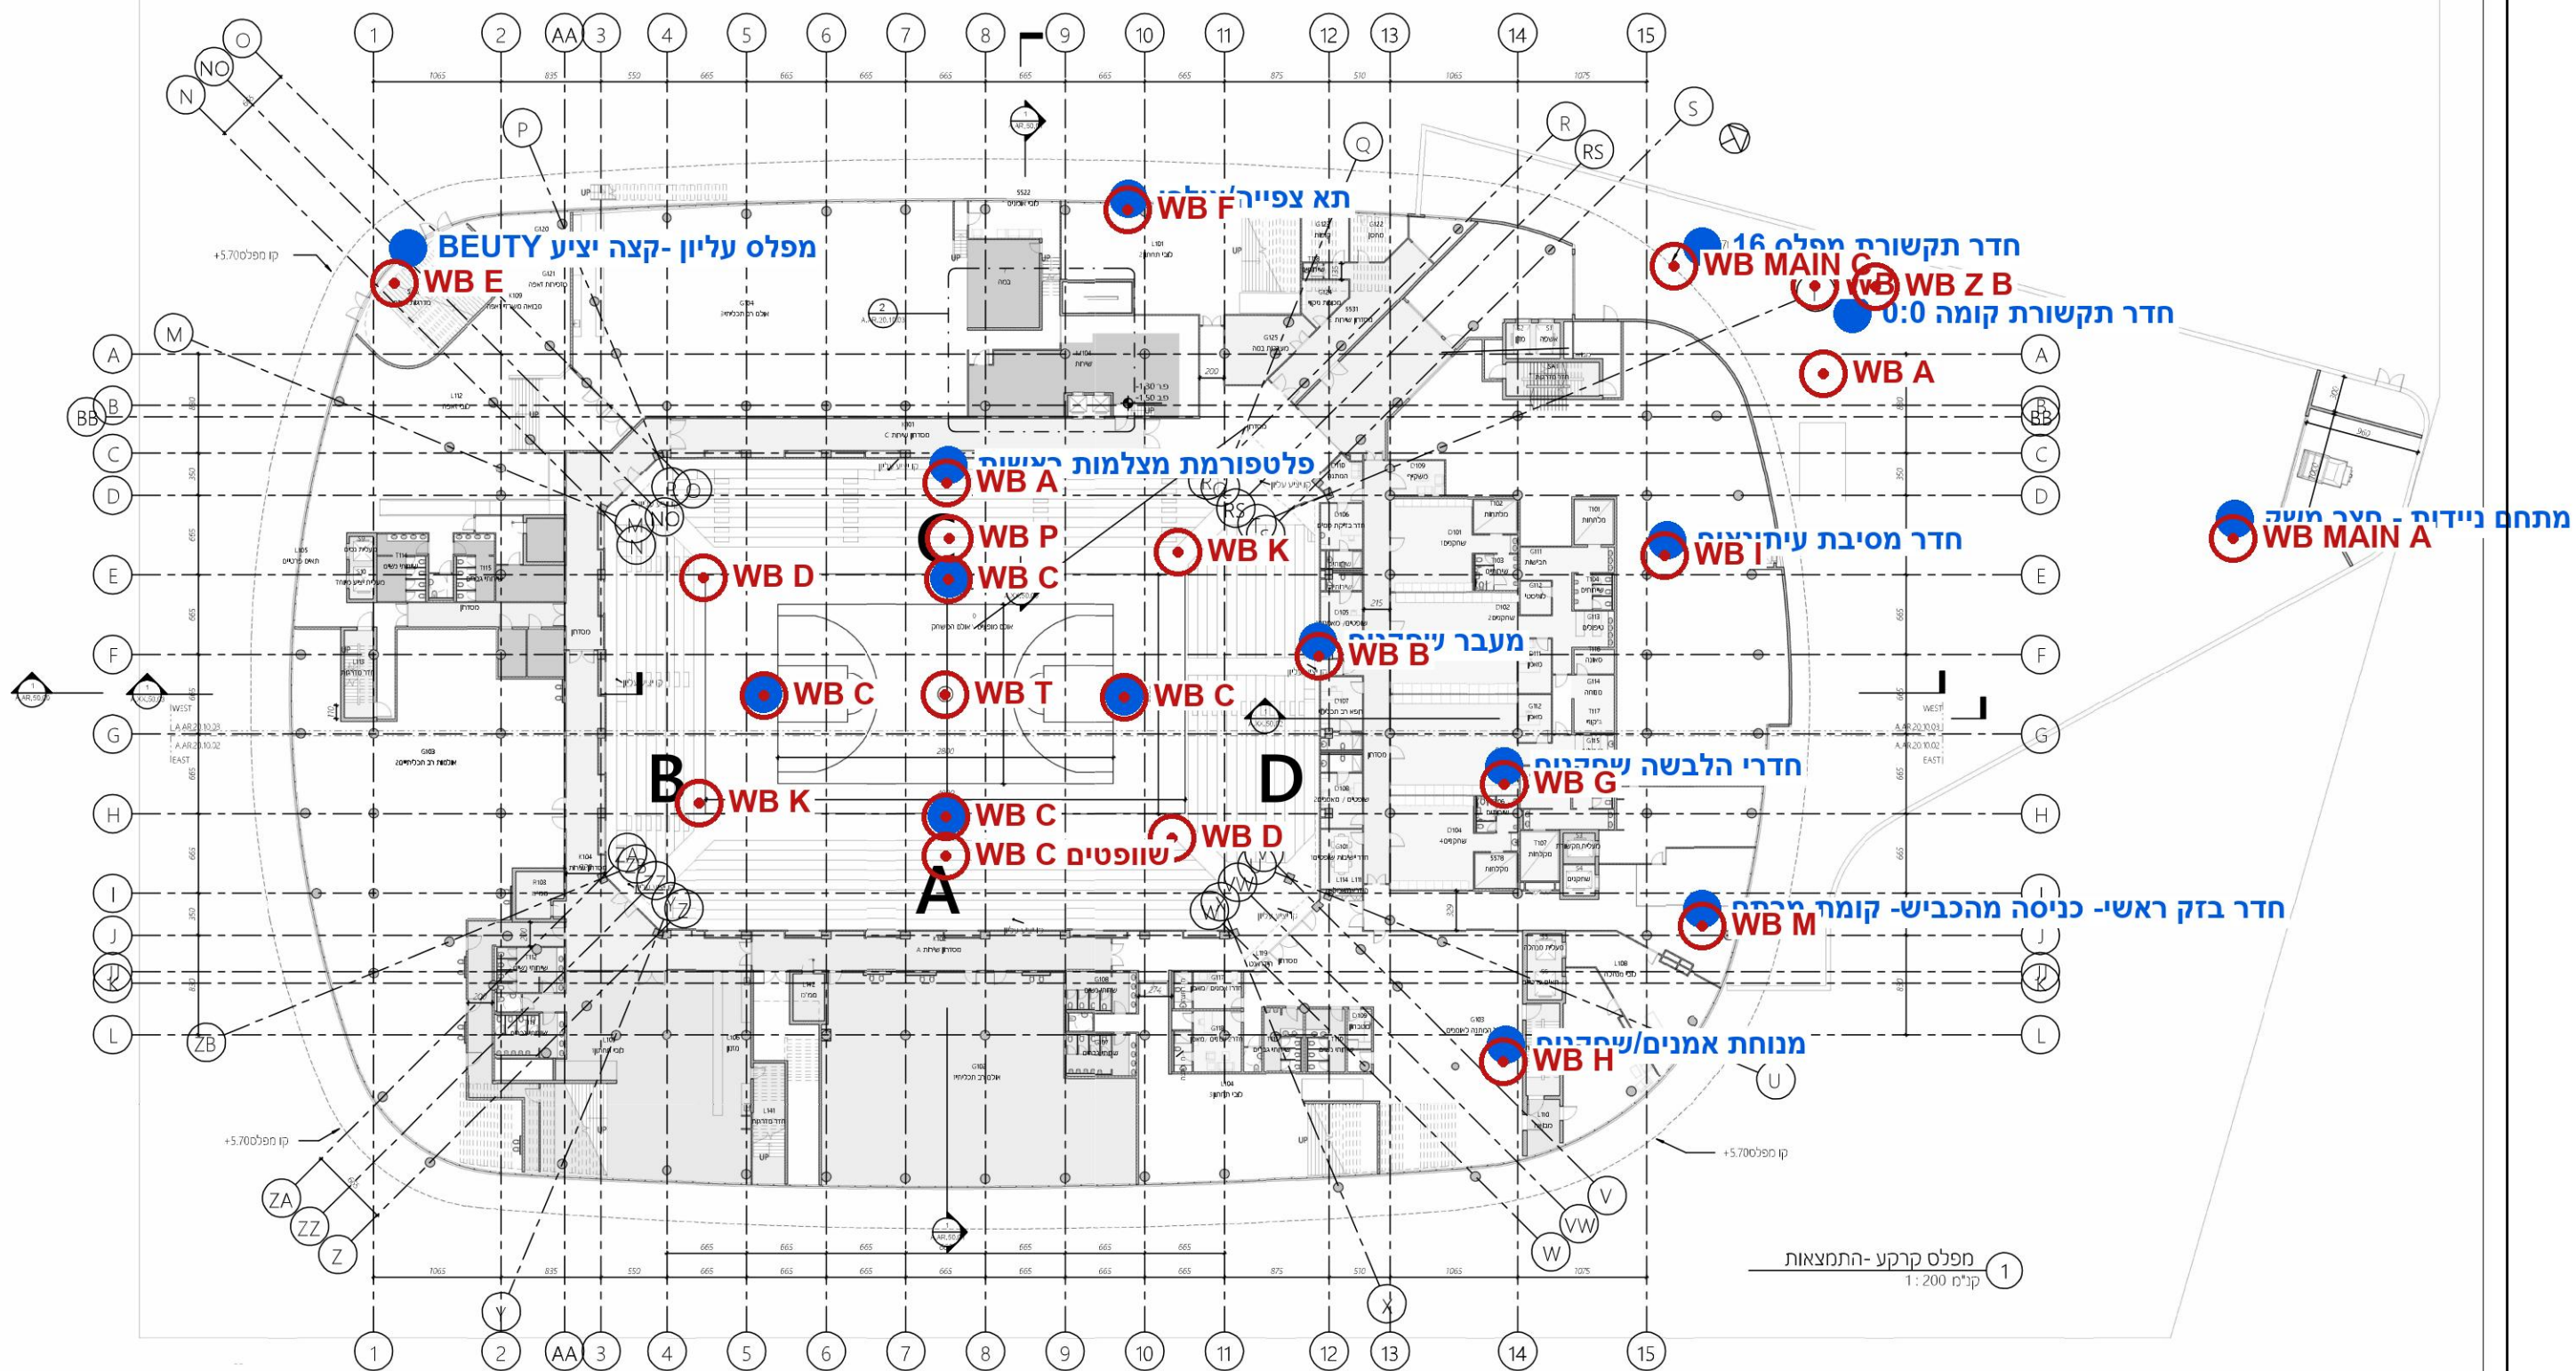

עיריית ראשל"צ



העת:

[illegible]

תפוצת גליונות - חכמן

[illegible]


הפצת מהדורות - כיצד

[illegible]

רשימת מתכננים

[illegible]

תוכנית מפרטת:

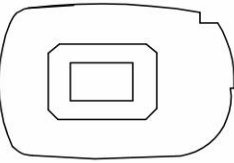

AR		הסדר מקום	תאריך Design Approved
אר.20.10.01		פרוייקט פרוייקט	אושר על ידי אושר על ידי
A.AR.20.10.01			
תוכנית התמצאות קומת פרקע			
	1 : 200	לפי כישור לחצה לצד	☒ ☐ ☐ ☐
	DD/MM/YYYY		



אורבך הלוי

AUERBACH HALEVY Architects & Engineers Ltd

-  Lobby A, 5th floor Shiraz building,
Ha-Yotzim St 3, Lod
 T:03-5465557 | F:03-5445950
 Mail@AH-arch.com
 @Auerbach_Halevy
 Facebook.com/AuerbachHalevy

VISIT OUR WEBSITE 

www.GAB-Arch.co.il
www.AH-Arch.com

